


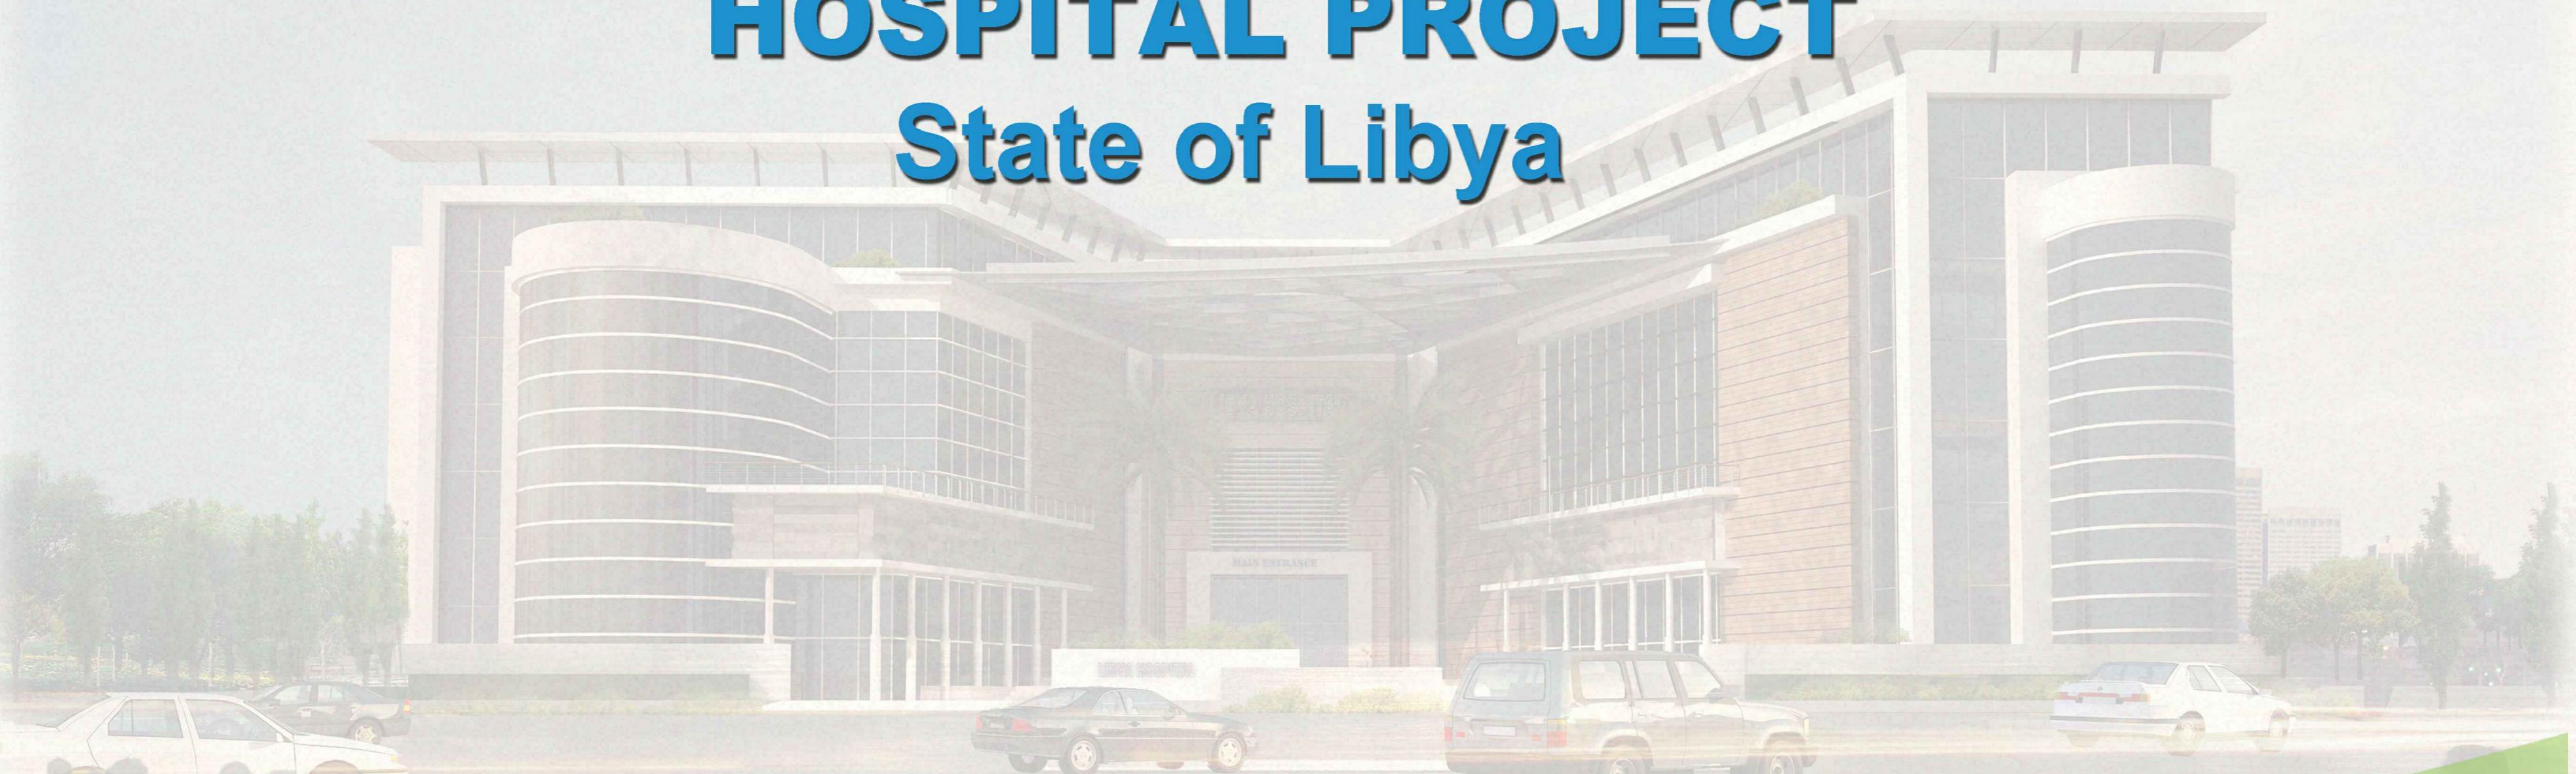

HOSPITAL PROJECT

State of Libya




ليبيا - طرابلس- عين زارة ص.ب : 301 تلفاكس : 00218213511223


Libya - Tripoli - Ain Zara P.O.B : 301 - TELFAX : 00218213511223




GROUND FLOOR PLAN

OVER ALL SITTING LAYOUT PLAN

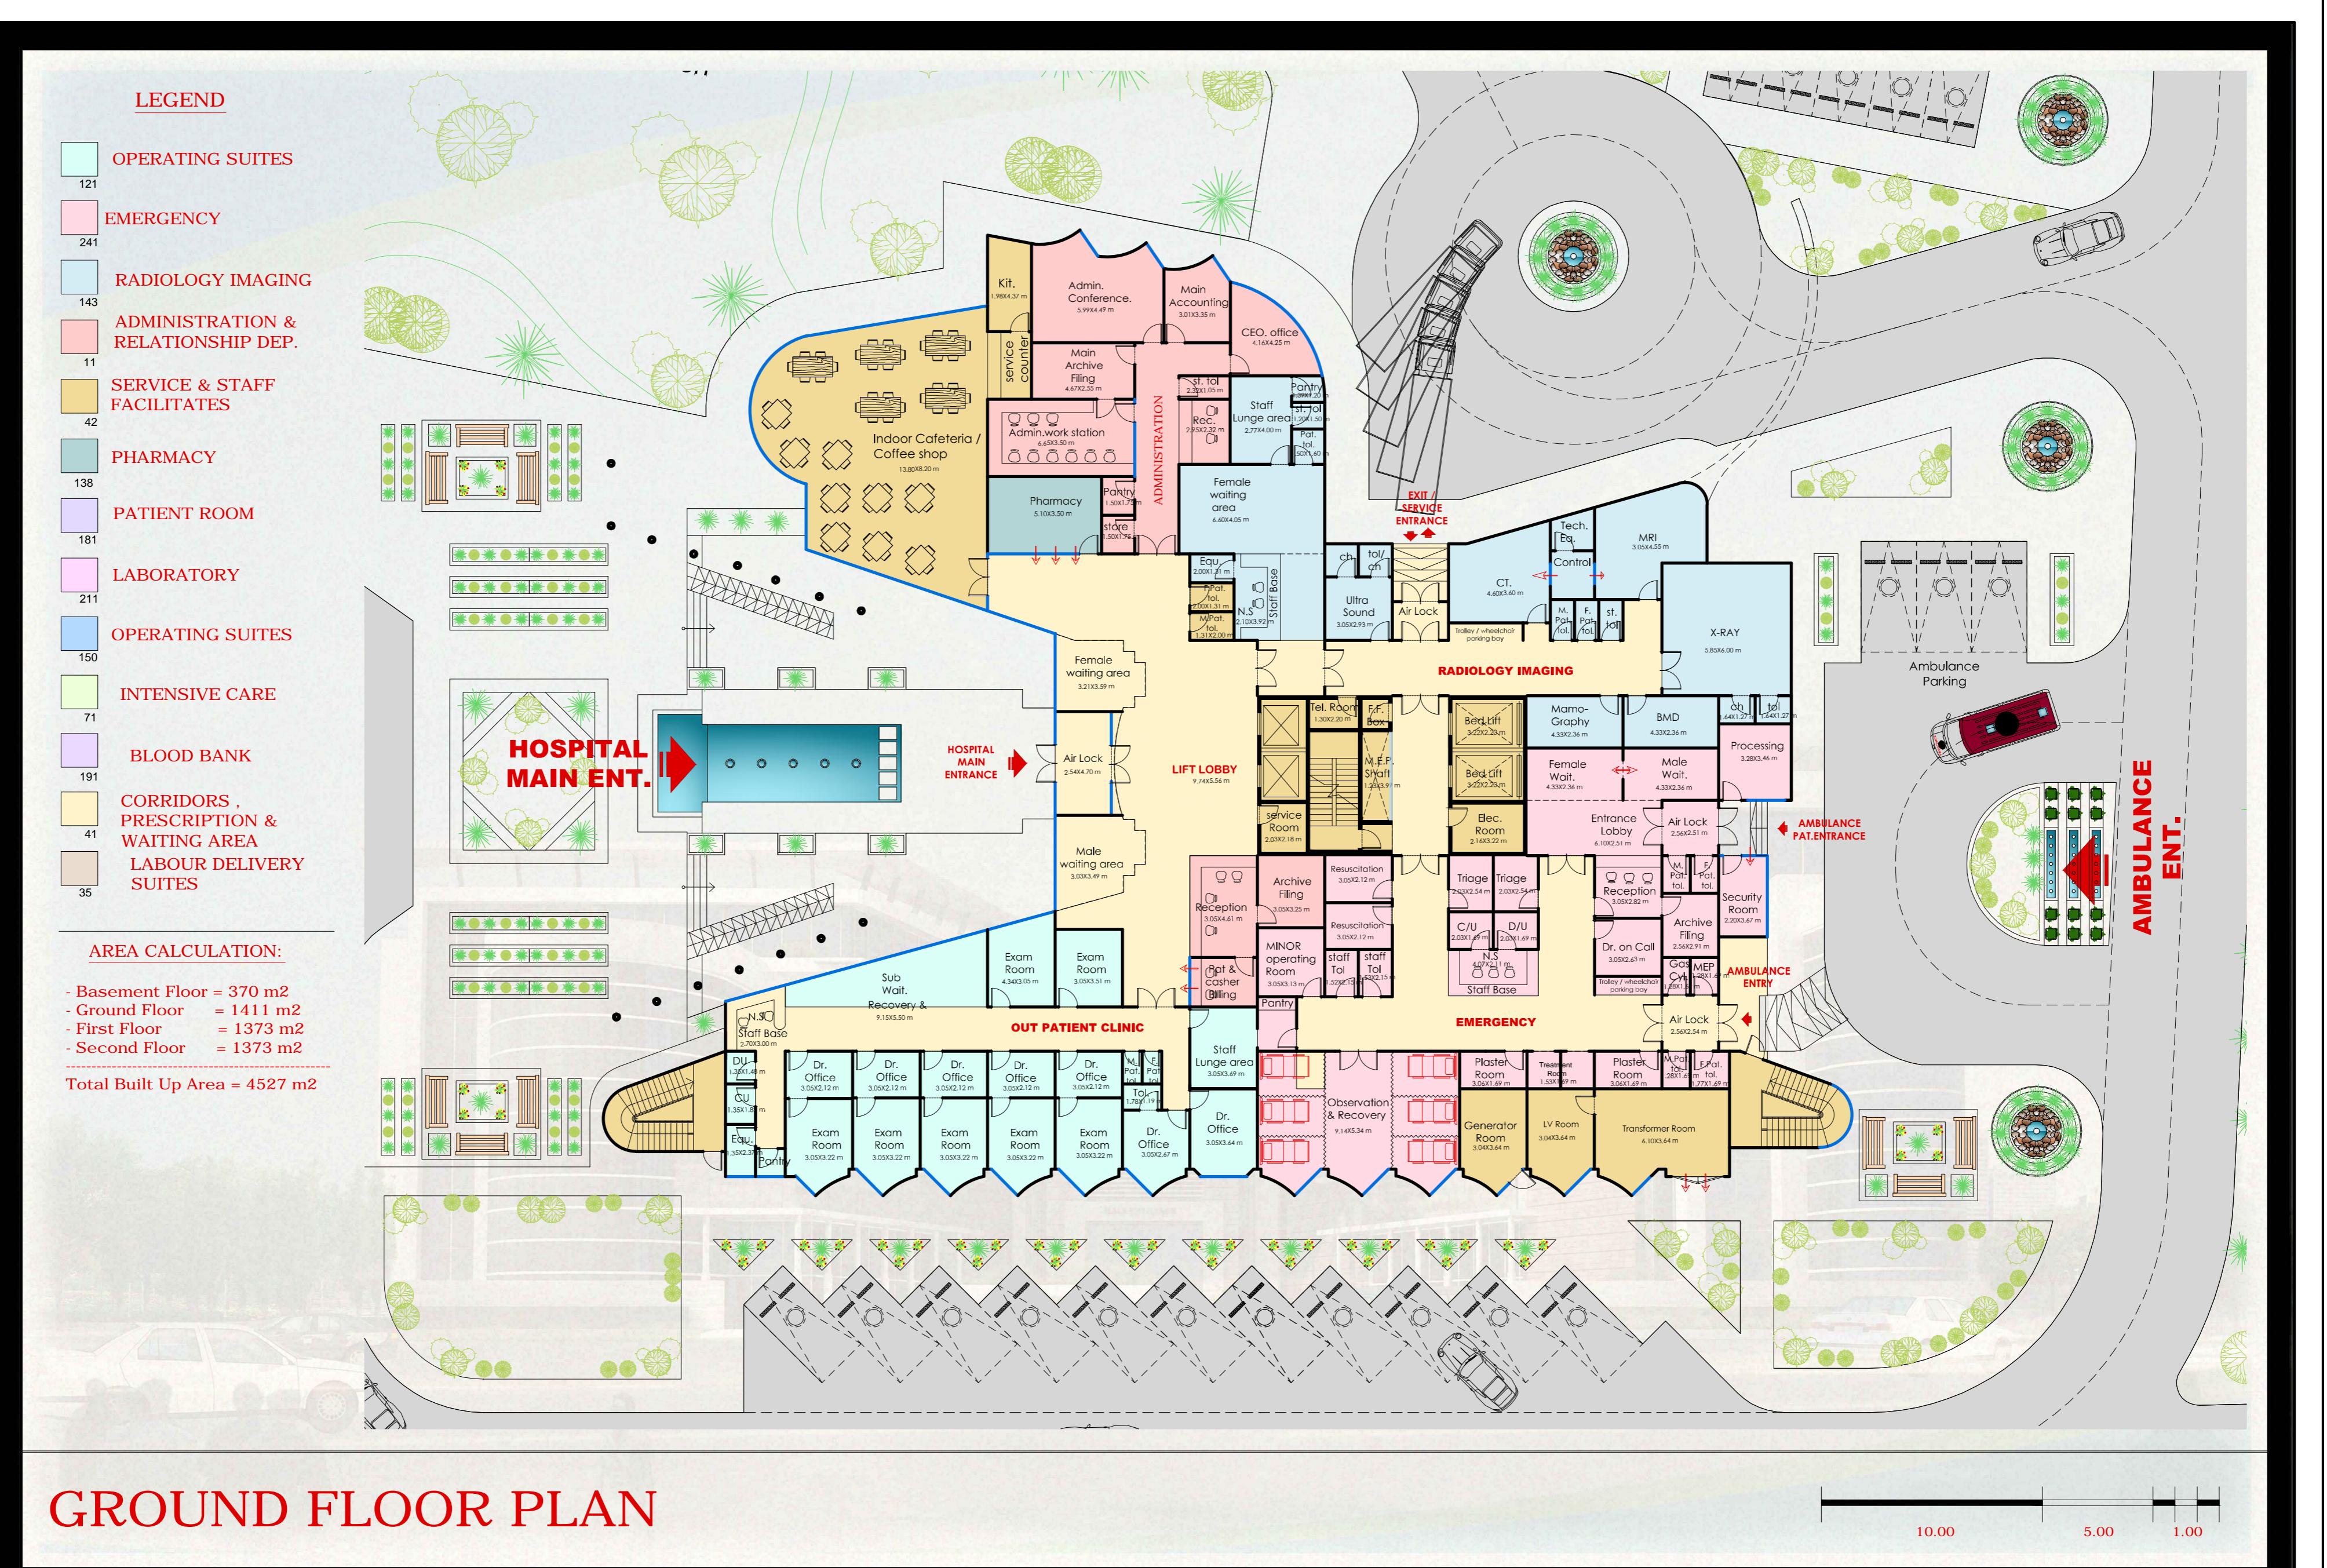

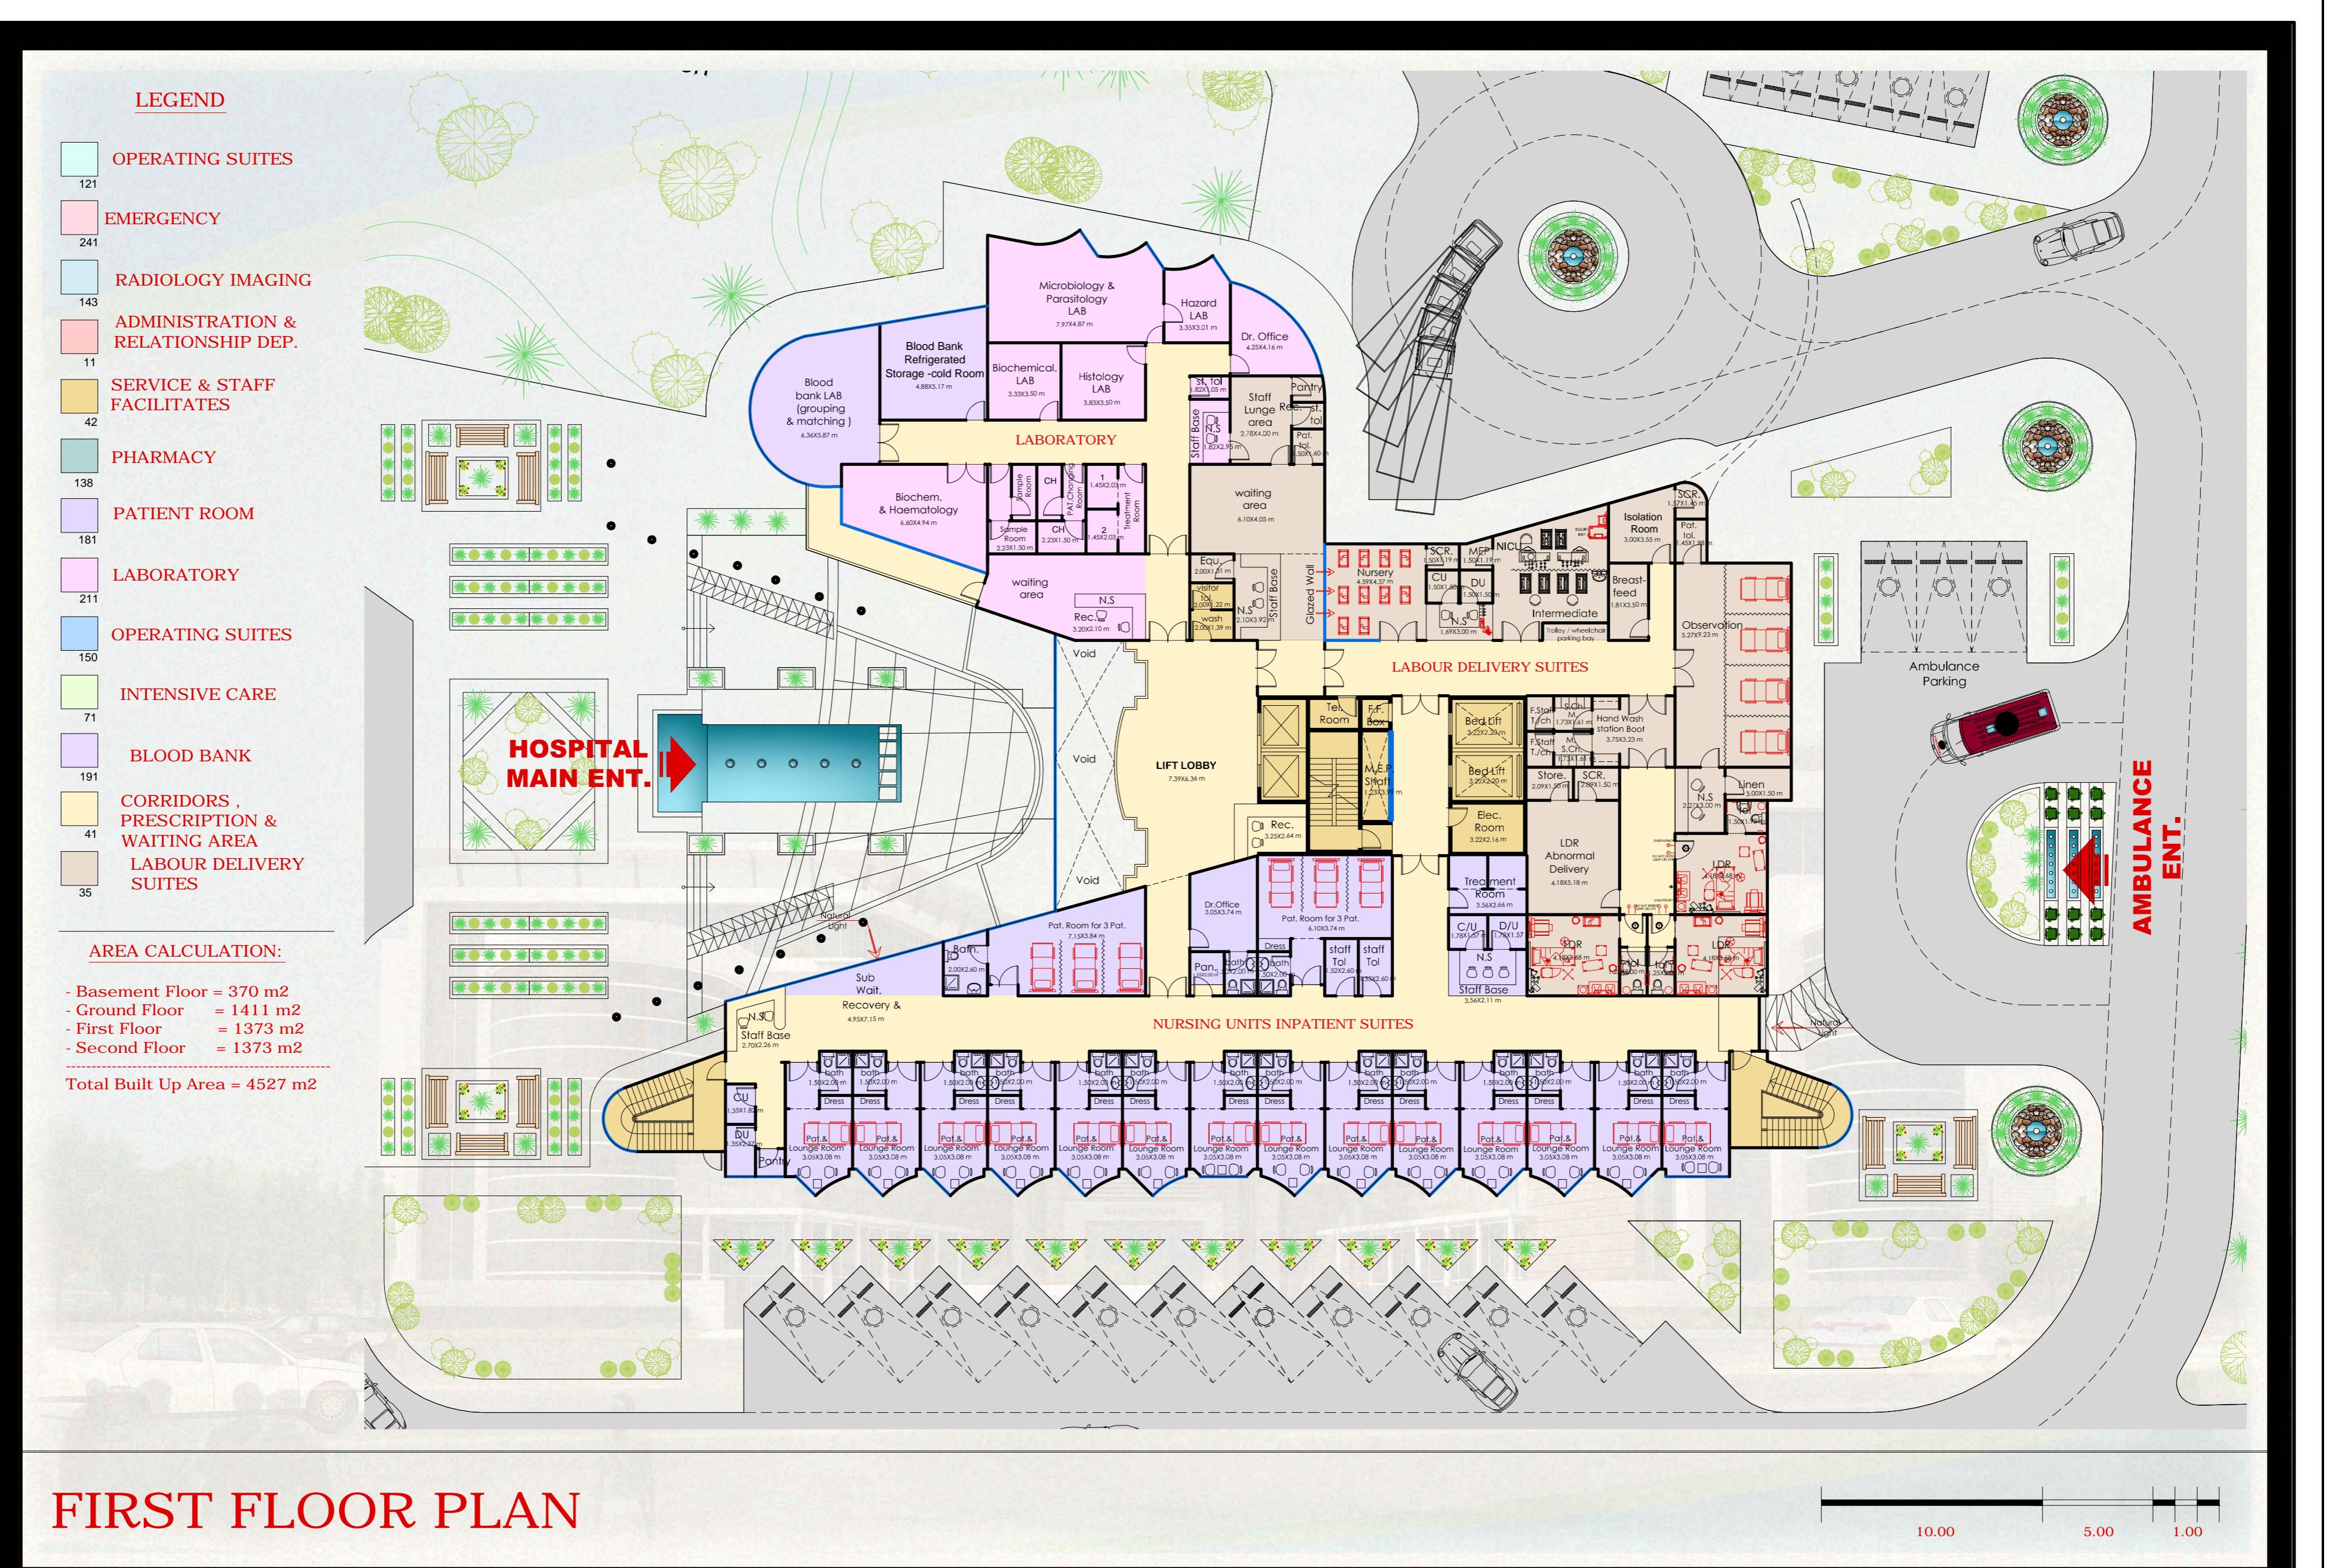

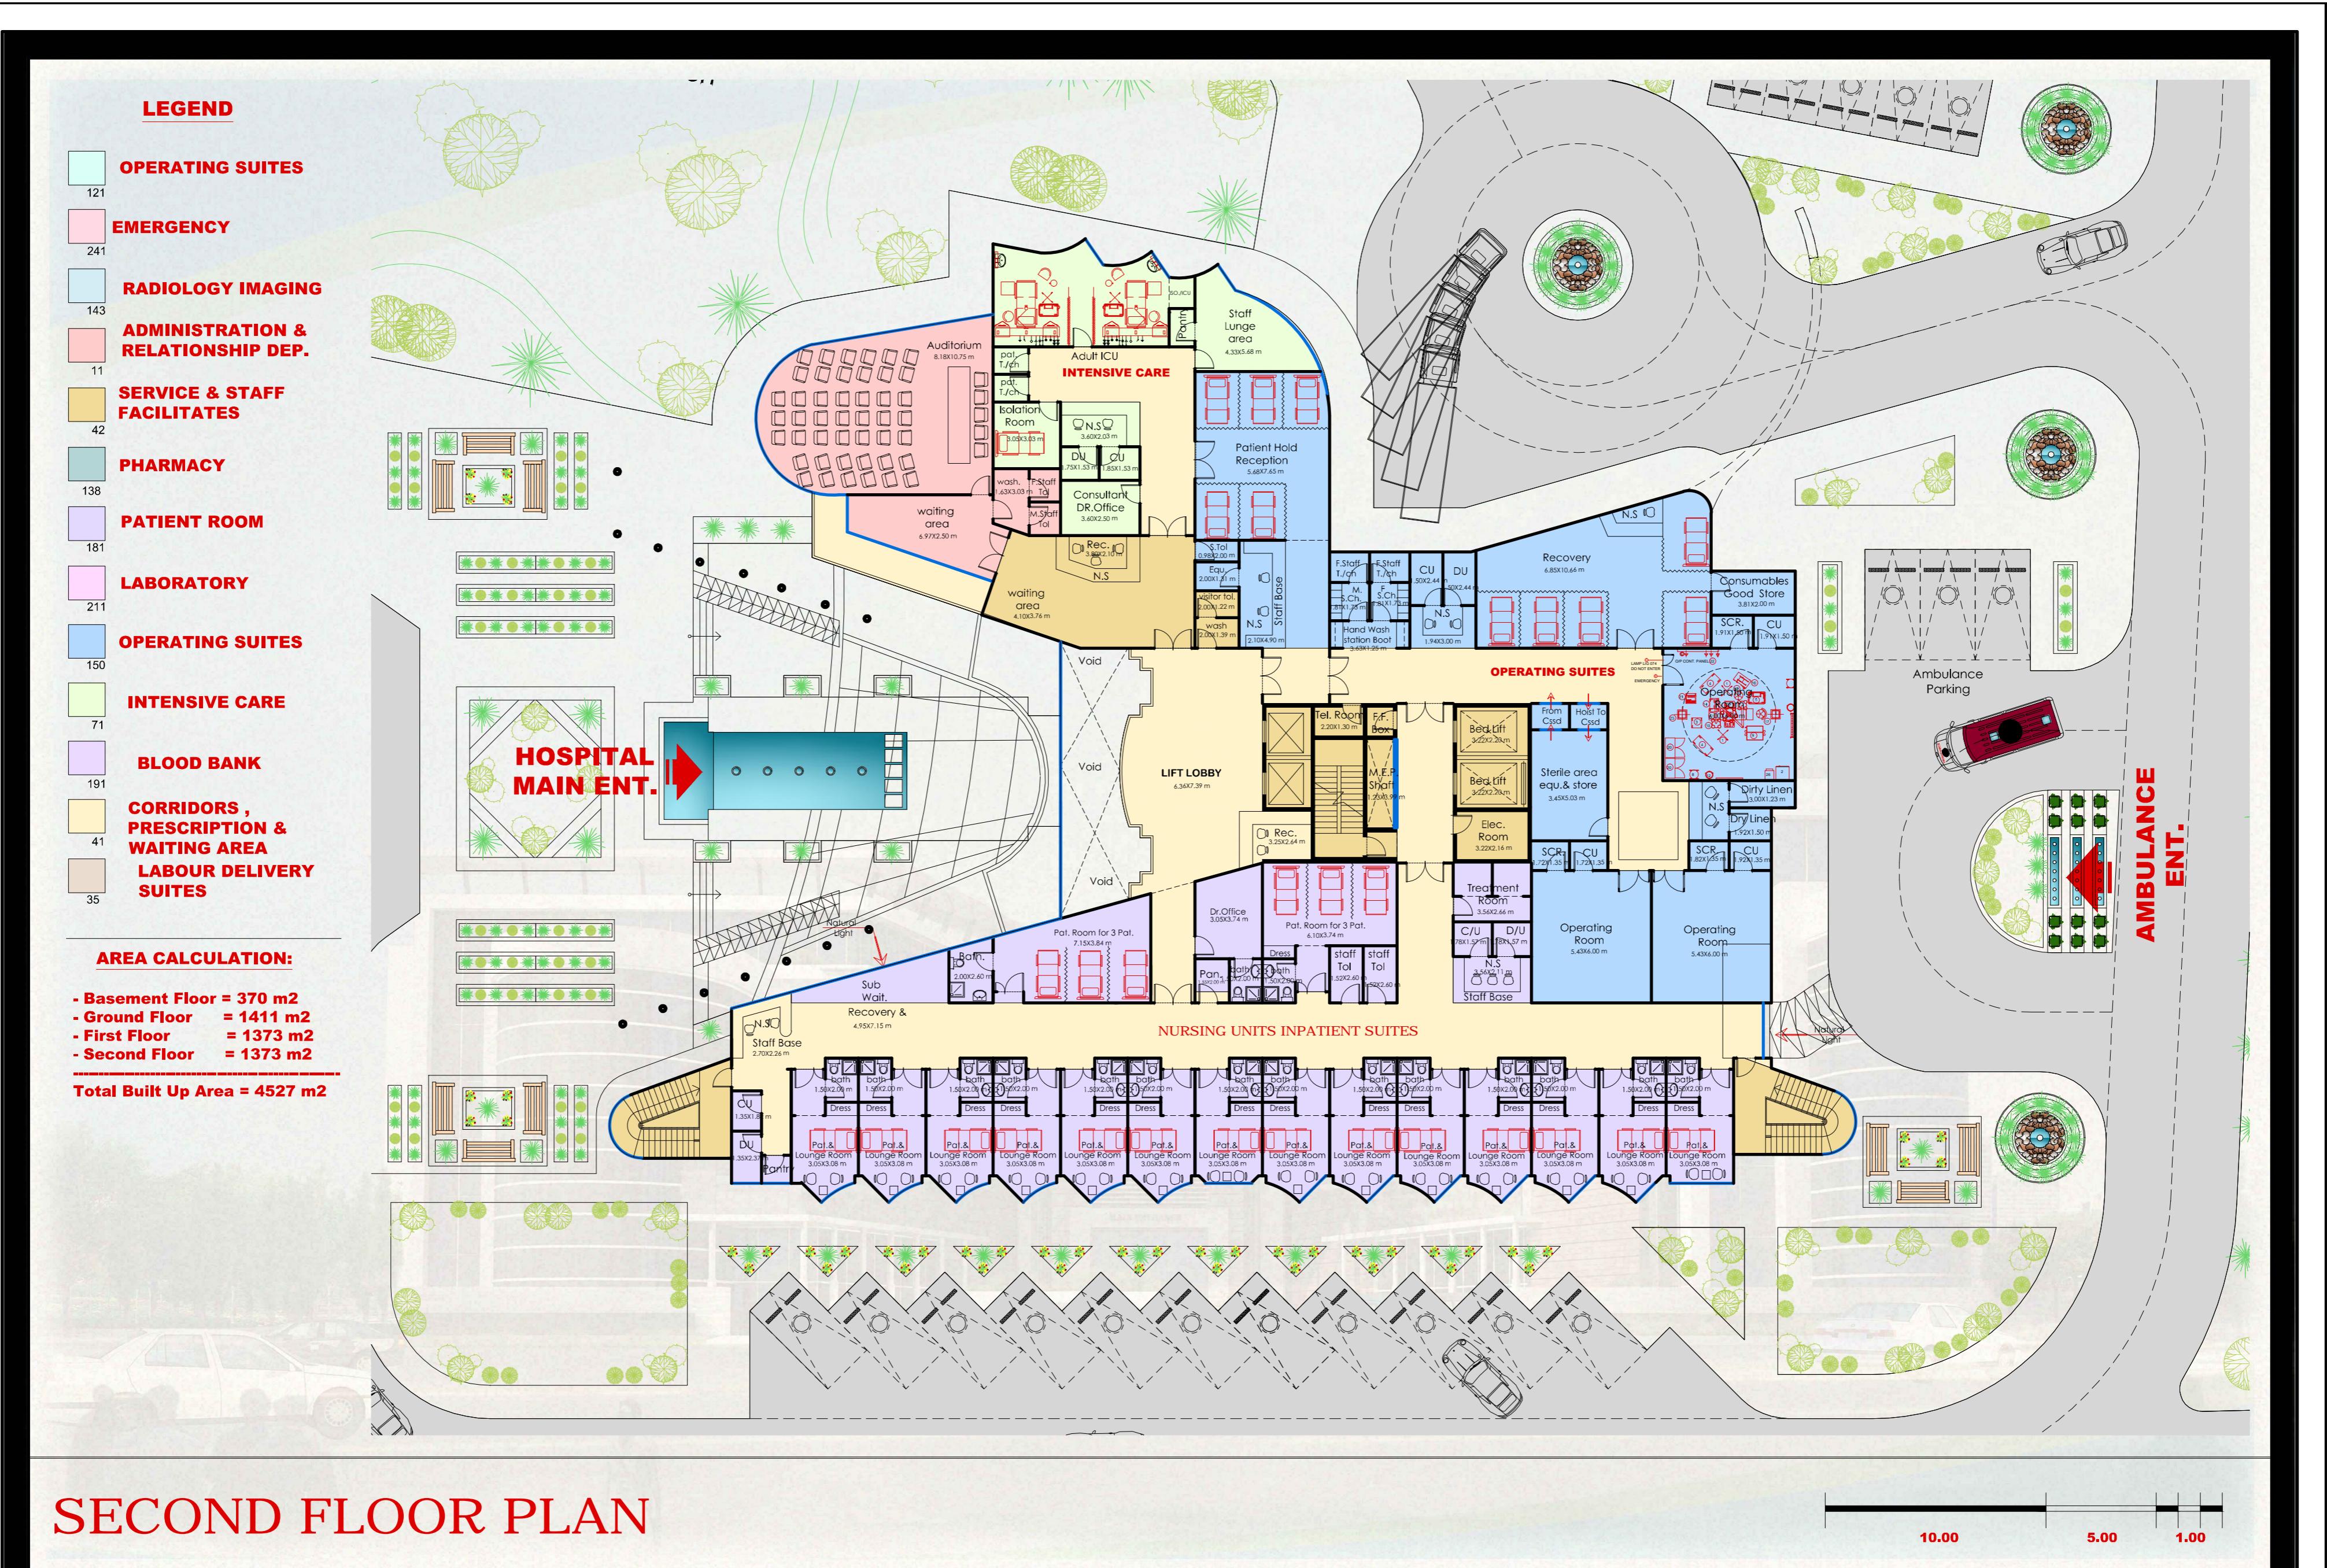


SECOND FLOOR PLAN

مِدِيَمْهَةُ لِيَبْرَا
للمقاولات والتطوير العقاري


MYMANA LIBYA
BUILDING CONTRACTING & REAL ESTATE DEVELOPMENT

HOSPITAL PROJECT (Bas+G+2 Floor)

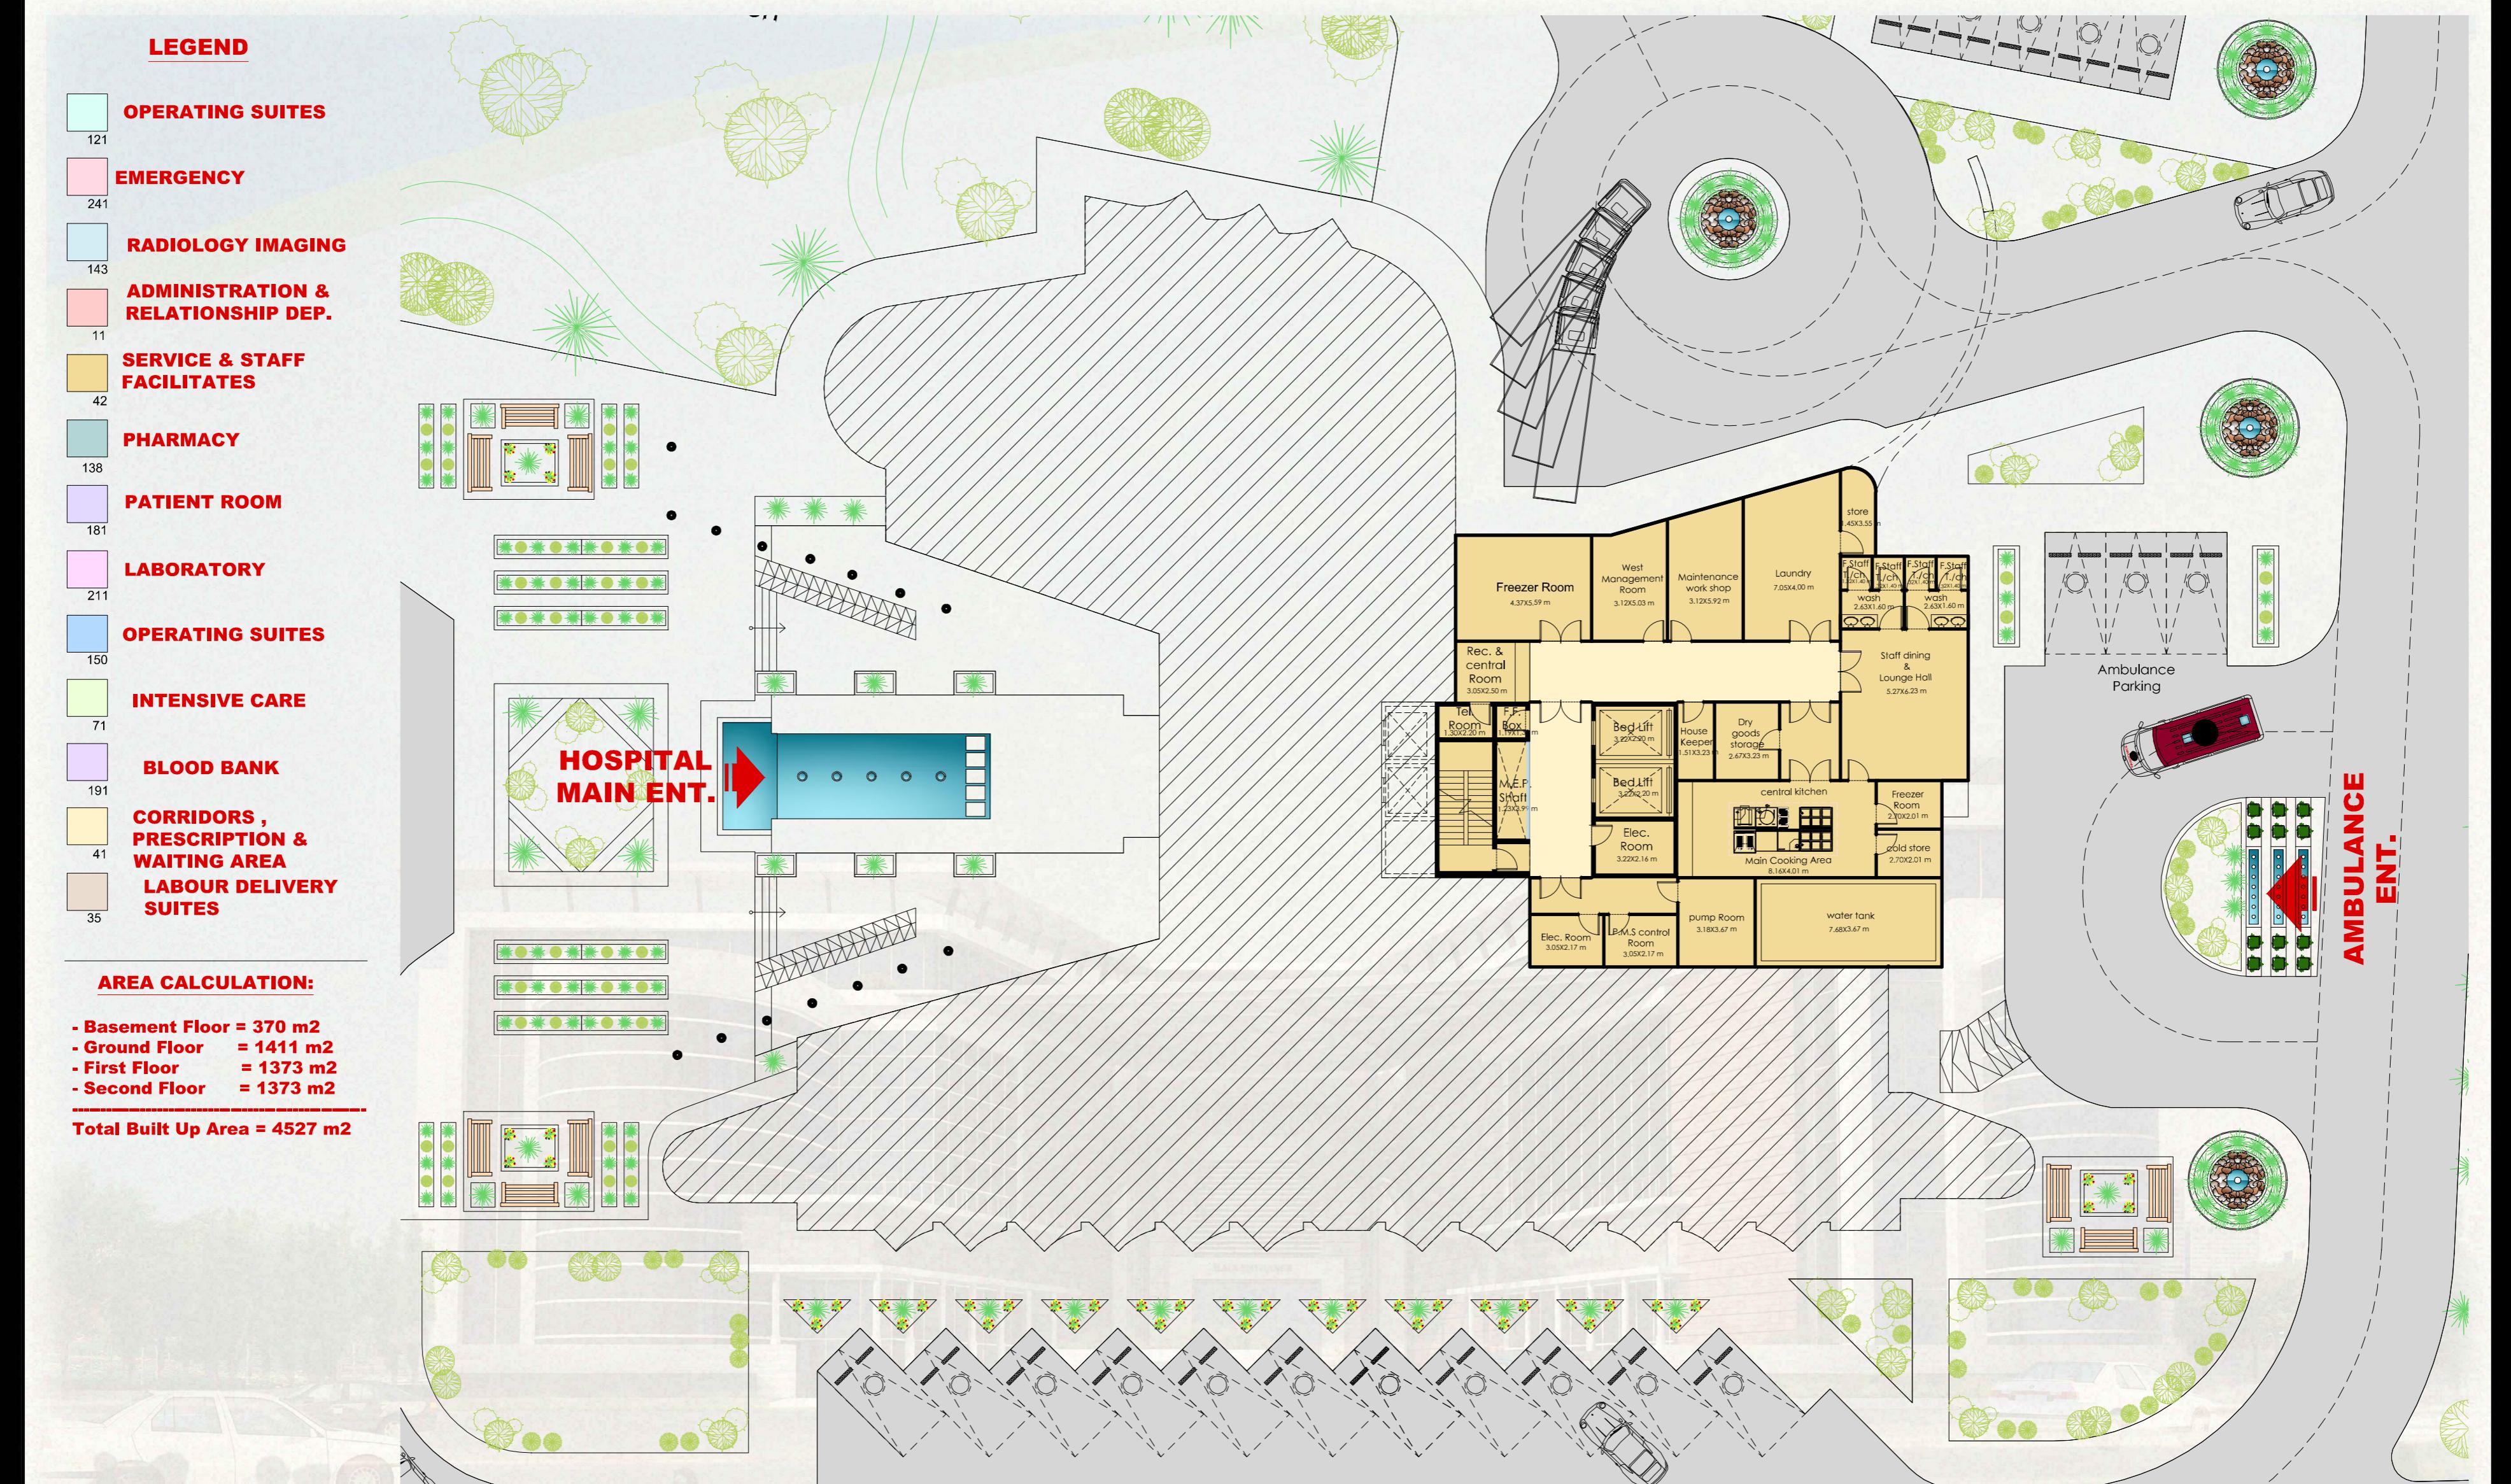

BASEMENT FLOOR PLAN

HOSPITAL PROJECT (Bas+G+2 Floor)

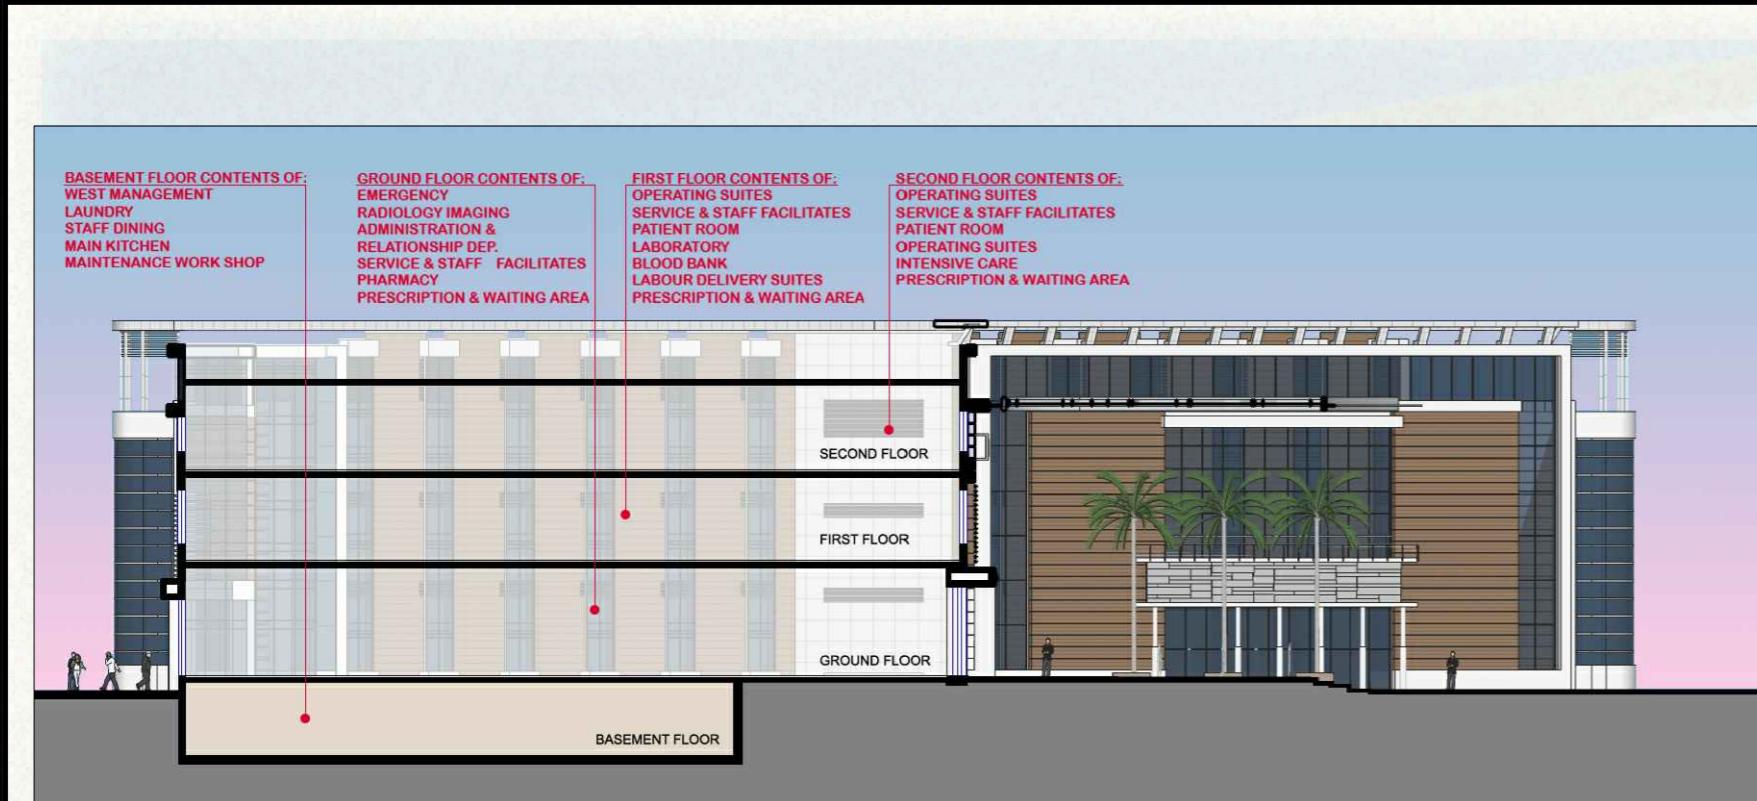


Main Section
N.T.S



Hospital Main Entrance lounge area
N.T.S



outpatient clinic sub wait area

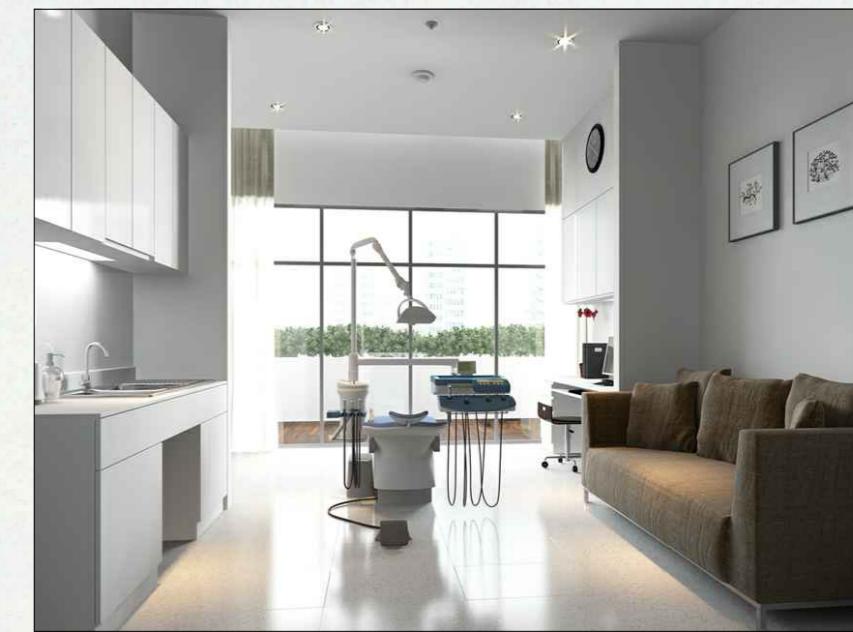

Dental outpatient clinic



Visitor Cafeteria



Nursing Station





Ground Floor Plan Key Plan




X-RAY Unit

FUNCTIONAL PART PLAN DETAILS .

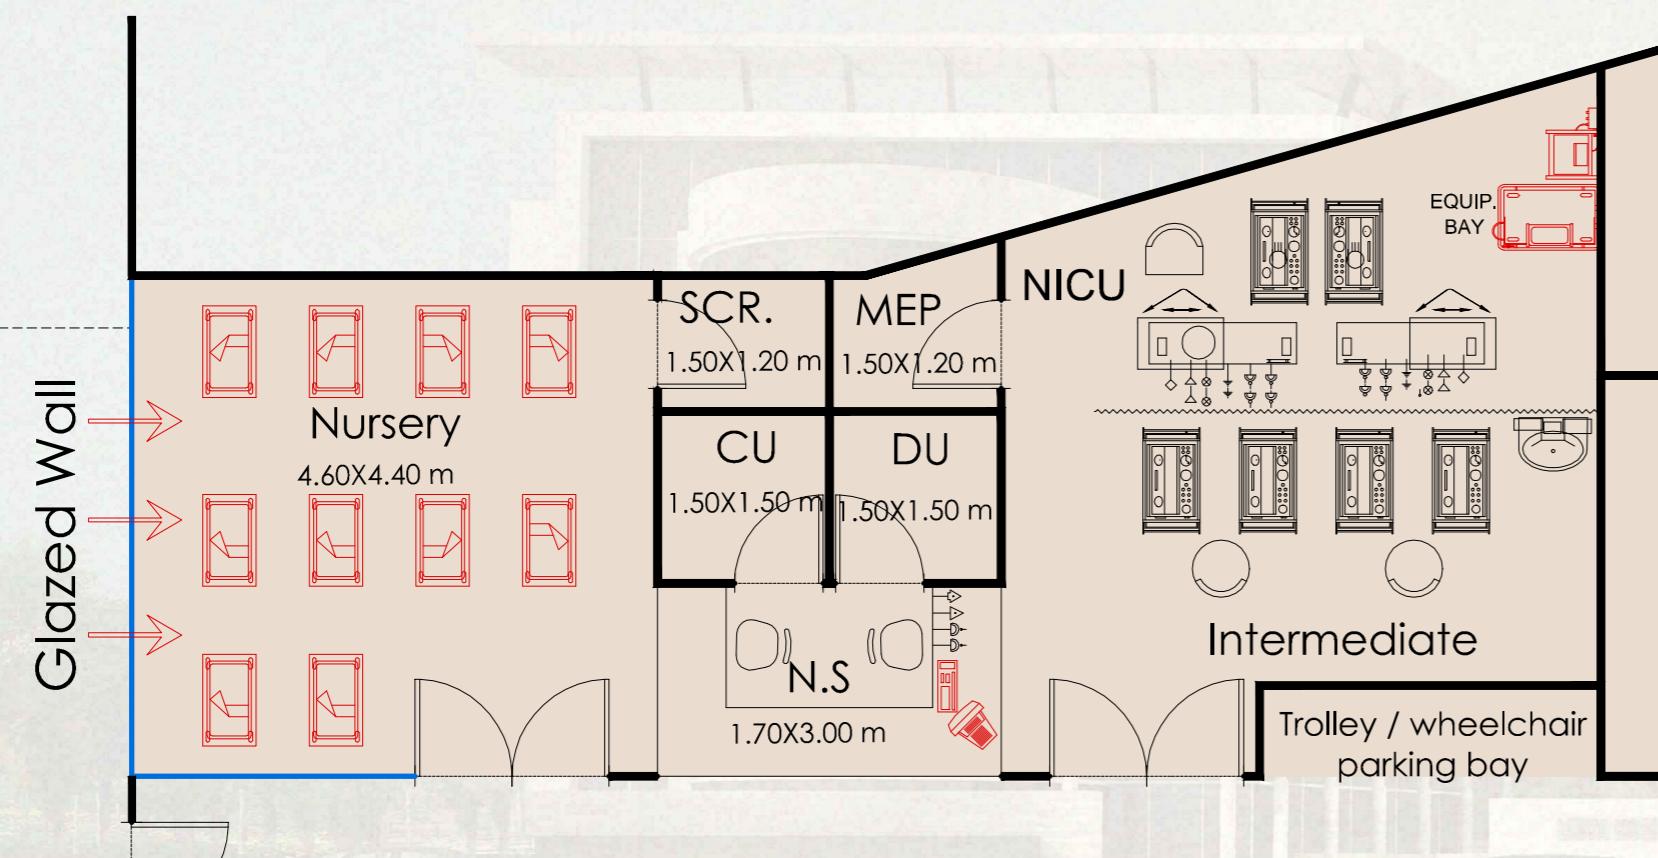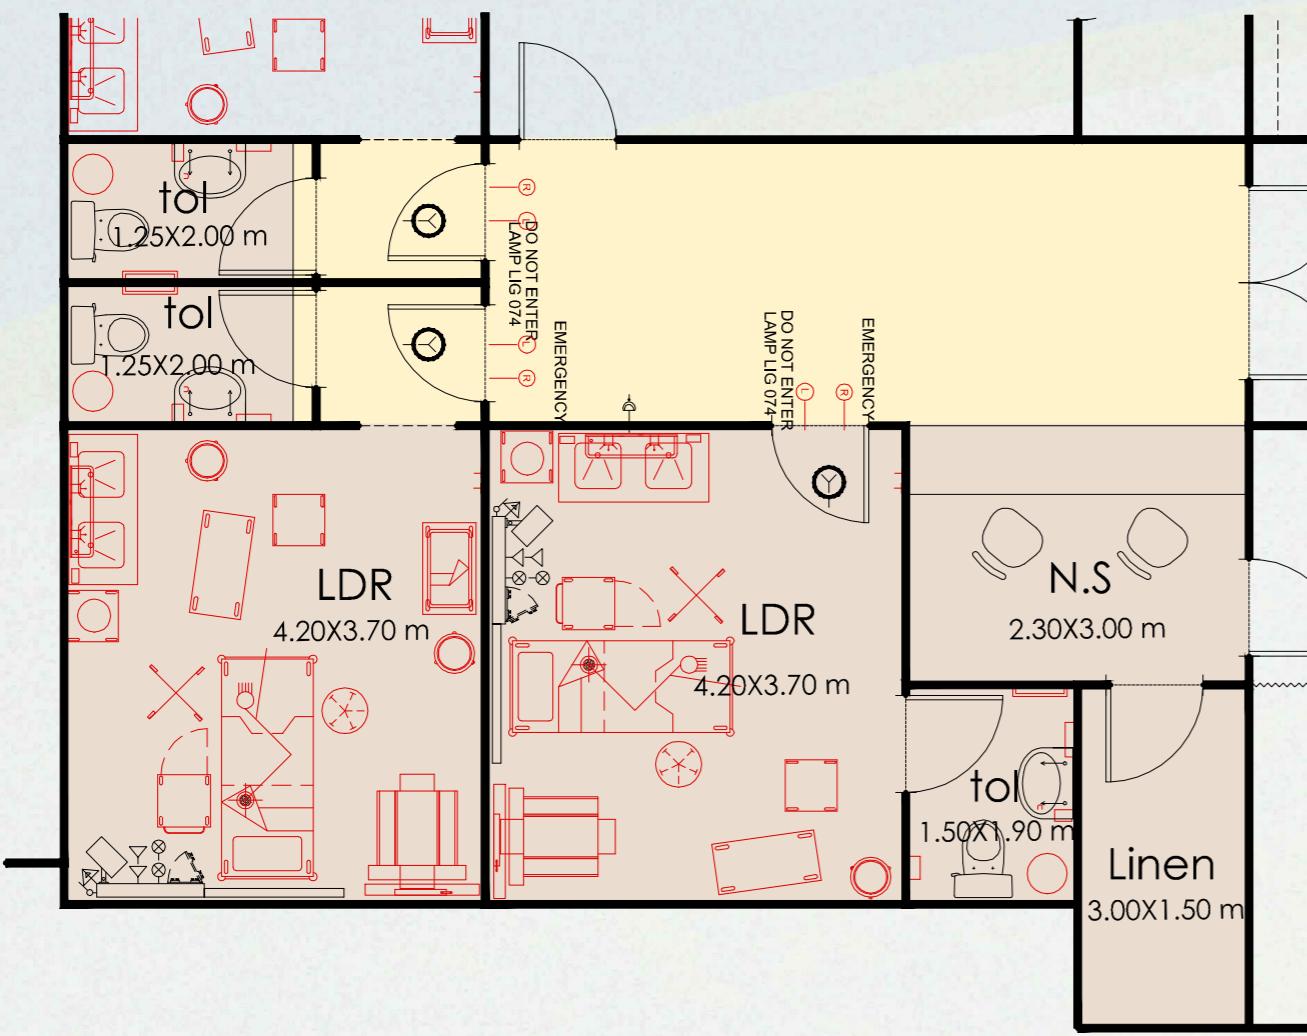


sample for interior design for units ..

FUNCTIONAL PART PLAN DETAILS .

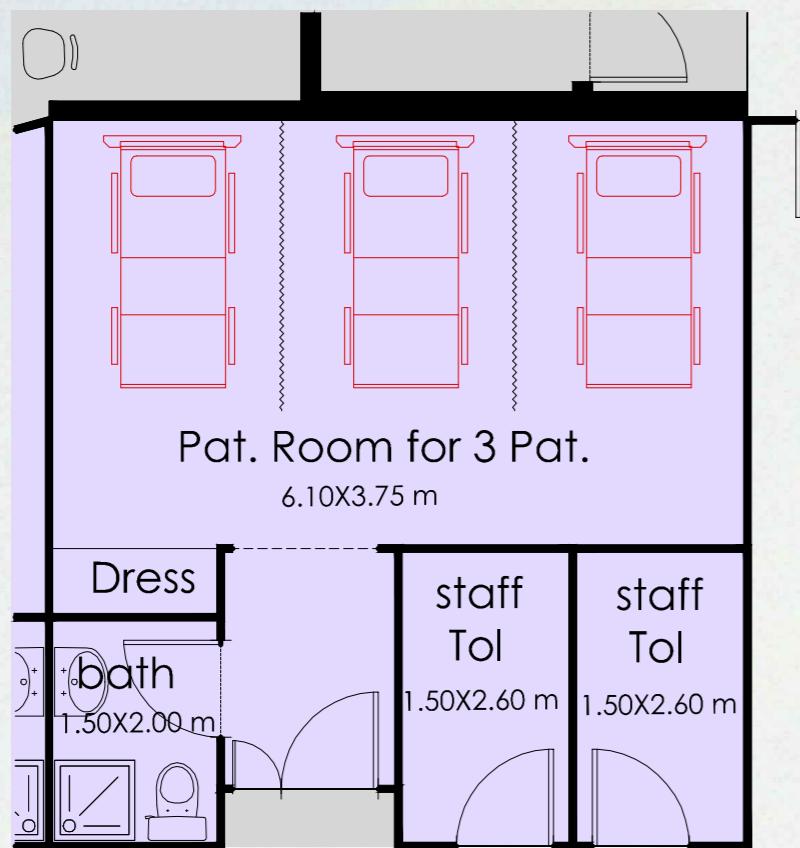

Nursing Units Inpatient Suite details (3 patients)

N.T.S

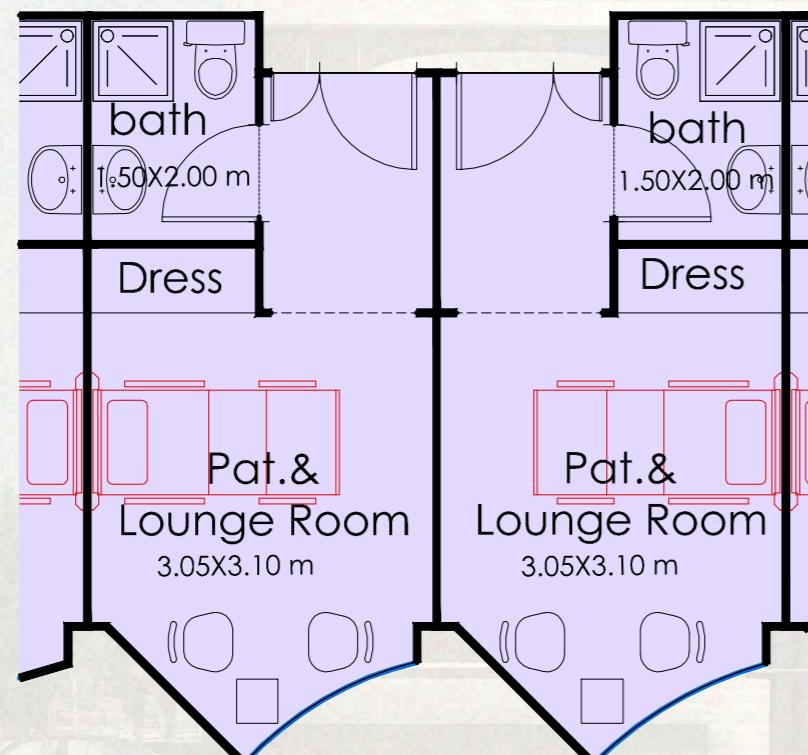

Nursing Units Inpatient Suite details (single patients)

N.T.S



single patients Room



single patients Room



single patients Room



single patients Room




Second Floor Plan Key Plan




sample for interior design for units ..

FUNCTIONAL PART PLAN DETAILS .

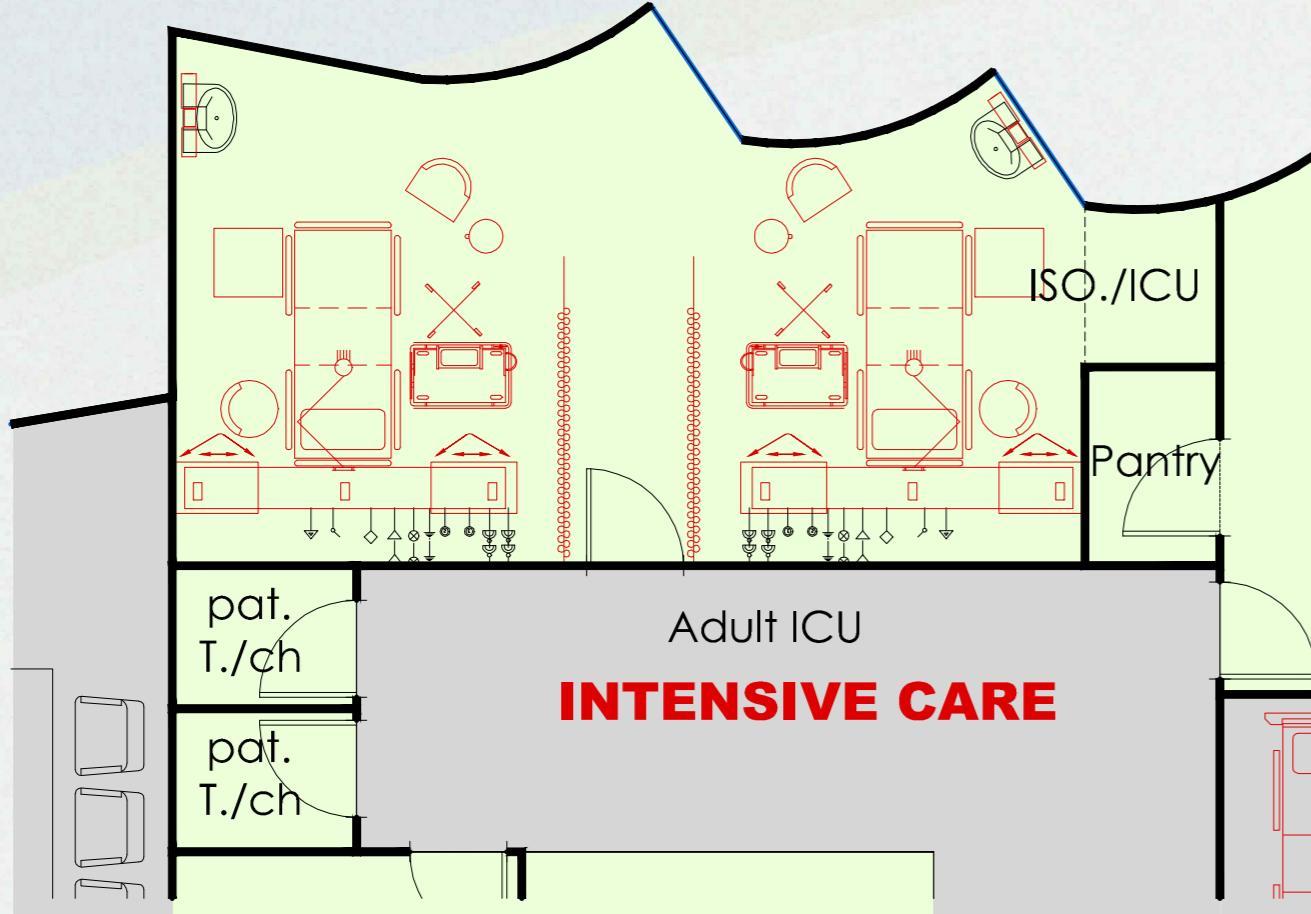

**Recovery Hall & nursing station Details
N.T.S**

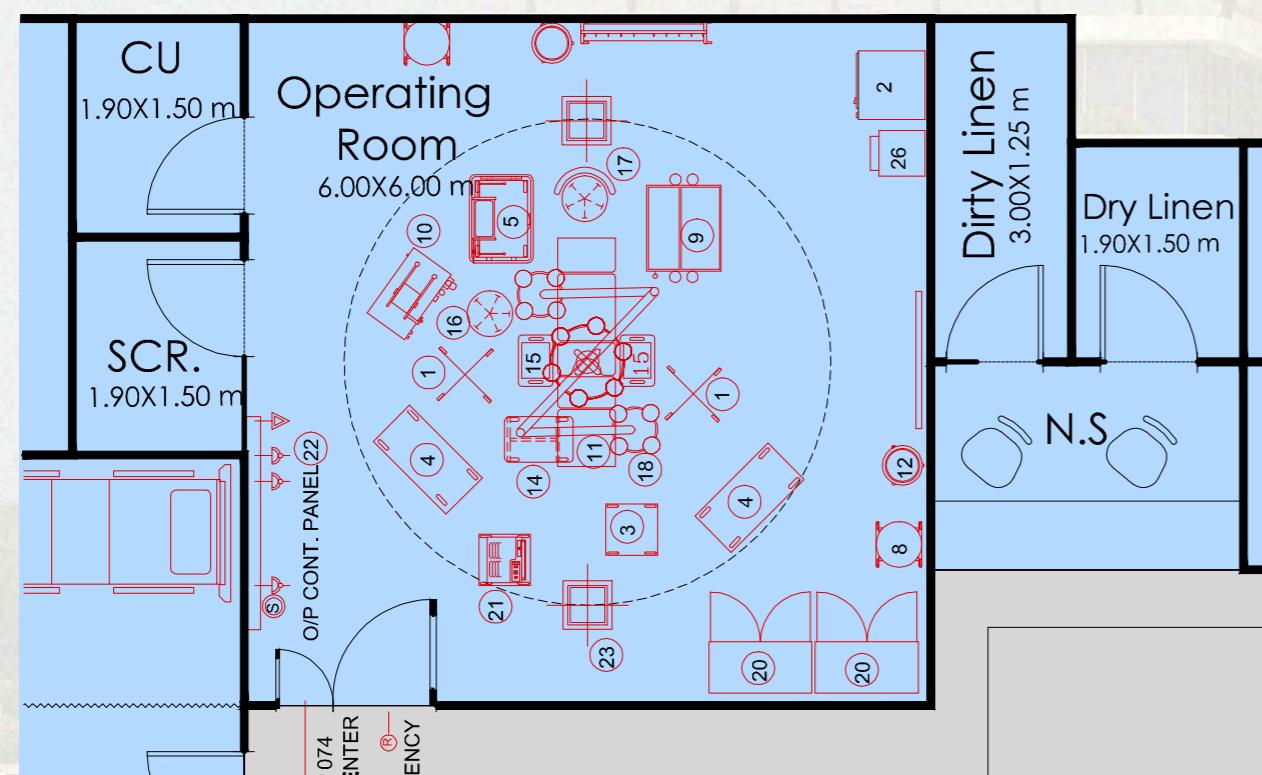


**Recovery Hall & nursing station Details
N.T.S**

FUNCTIONAL PART PLAN DETAILS .



Operating Room

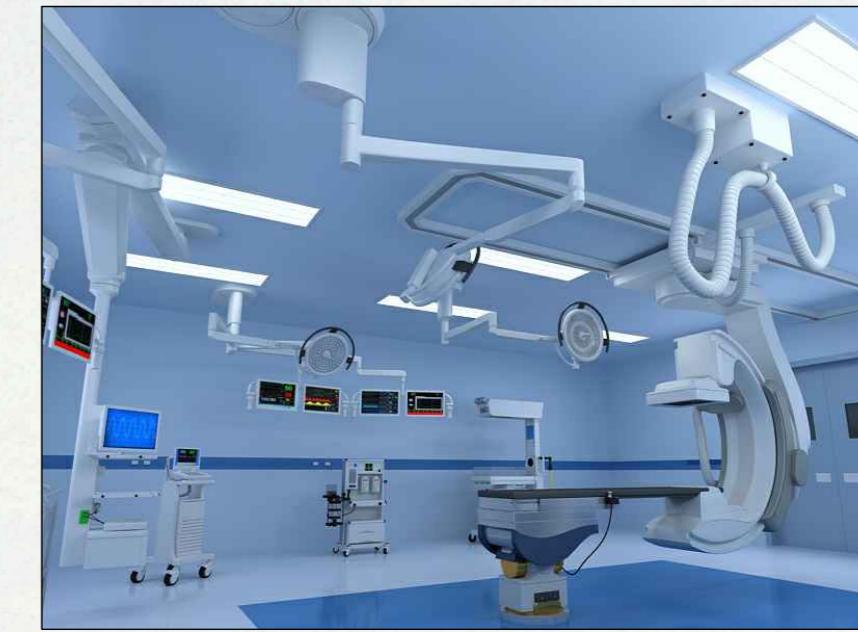

Operating Room



Operating Room



Intensive Care Area



Second Floor Plan Key Plan



sample for interior design for units ..




FRONT ELEVATION



RIGHT ELEVATION



REAR ELEVATION

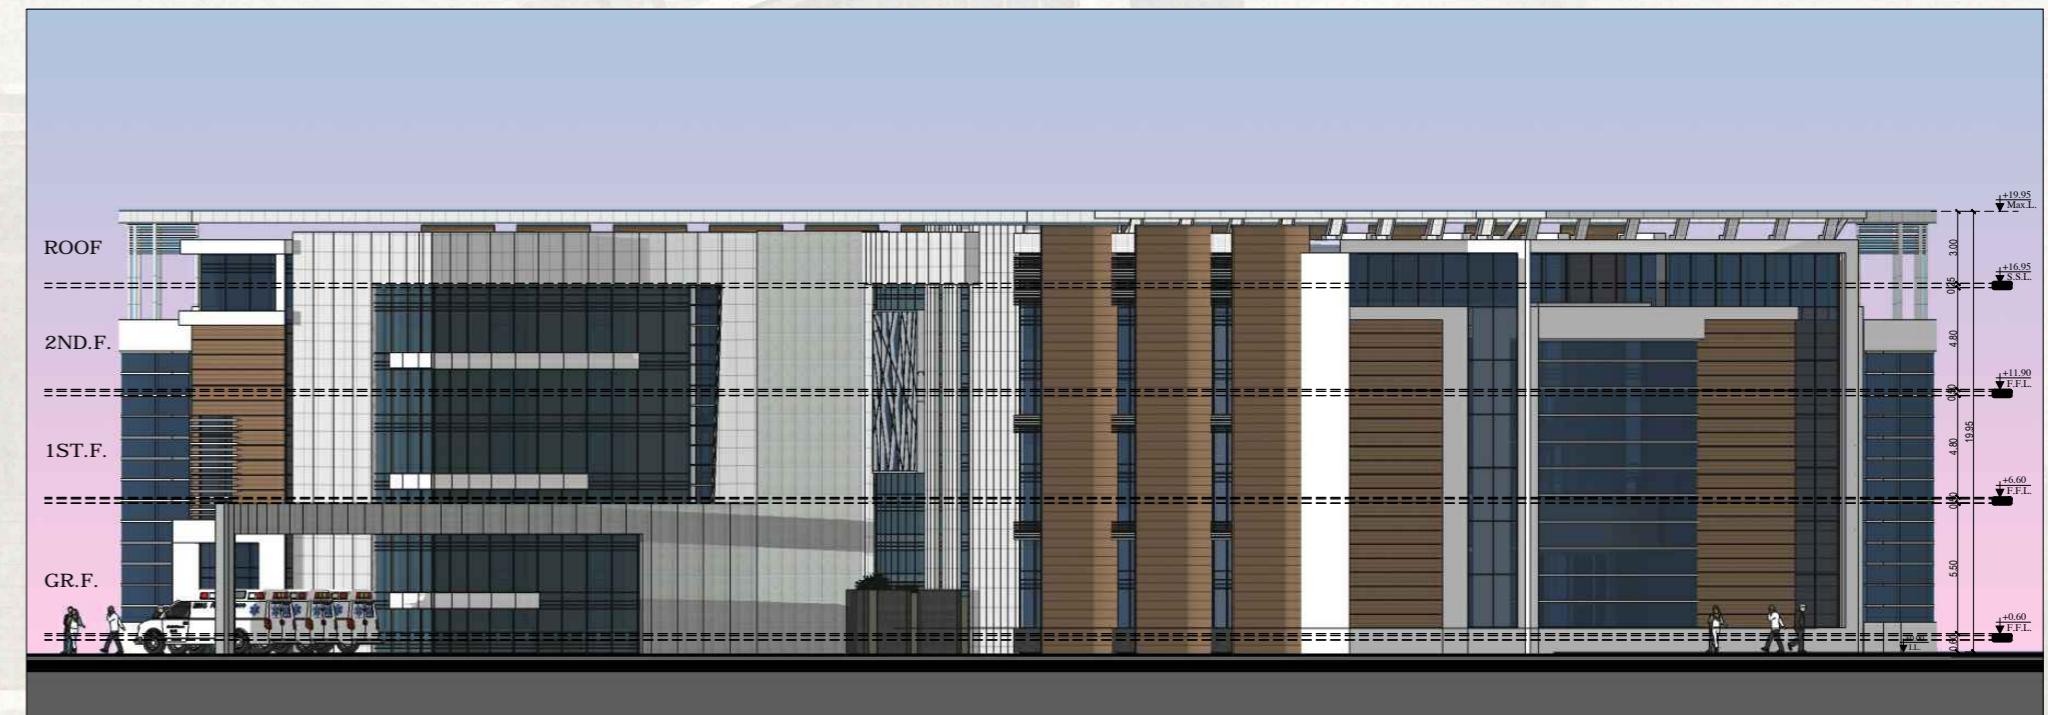


LEFT ELEVATION

ELEVATIONS







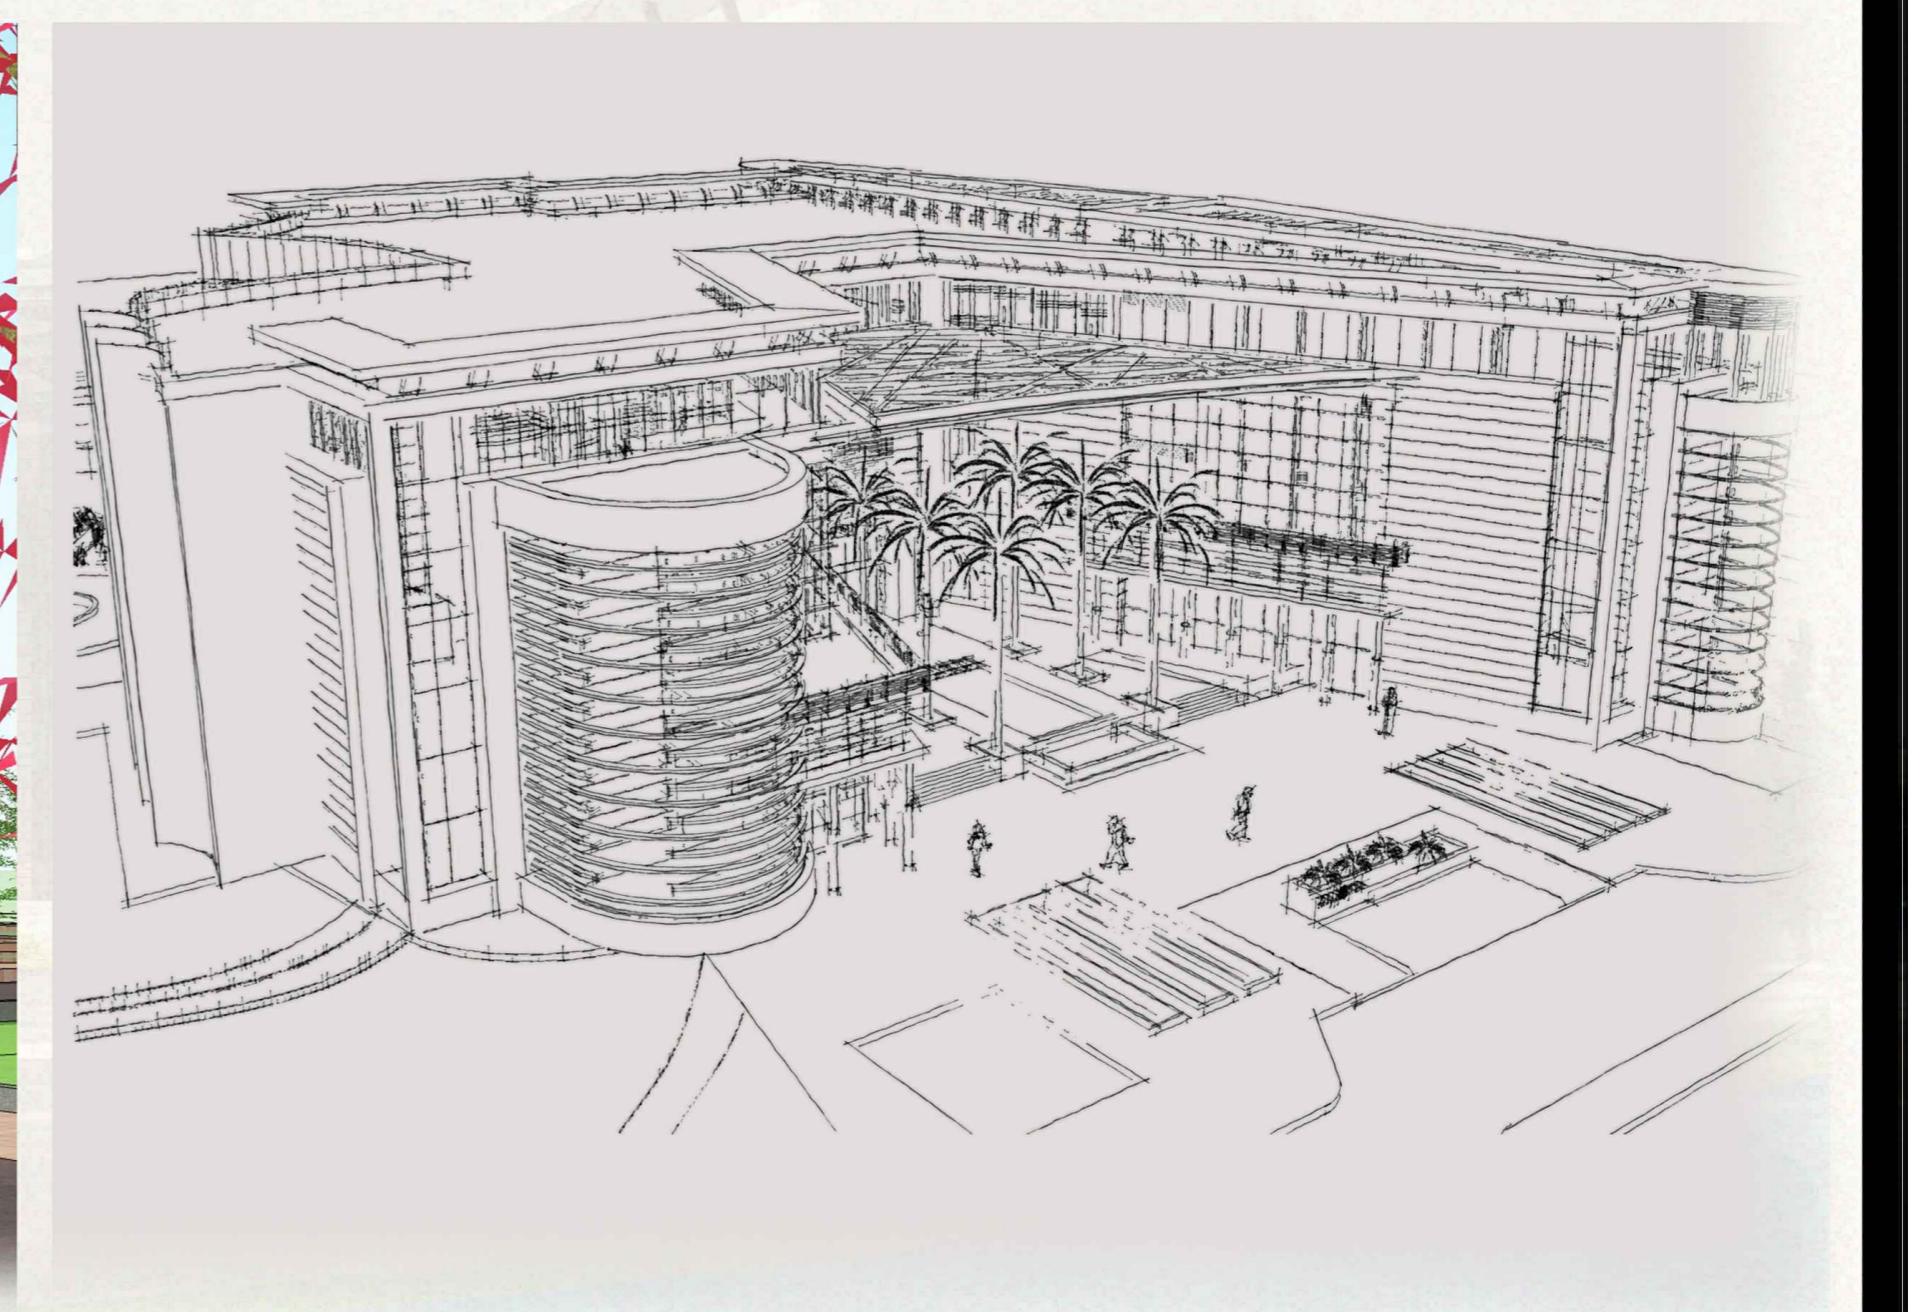



مِيَمَّا لِبْيَا



MYMANA LIBYA
BUILDING CONTRACTING & REAL ESTATE DEVELOPMENT

HOSPITAL PROJECT (Bas+G+2 Floor)